
DEPTH 1261 from internal dims (site total 1284)

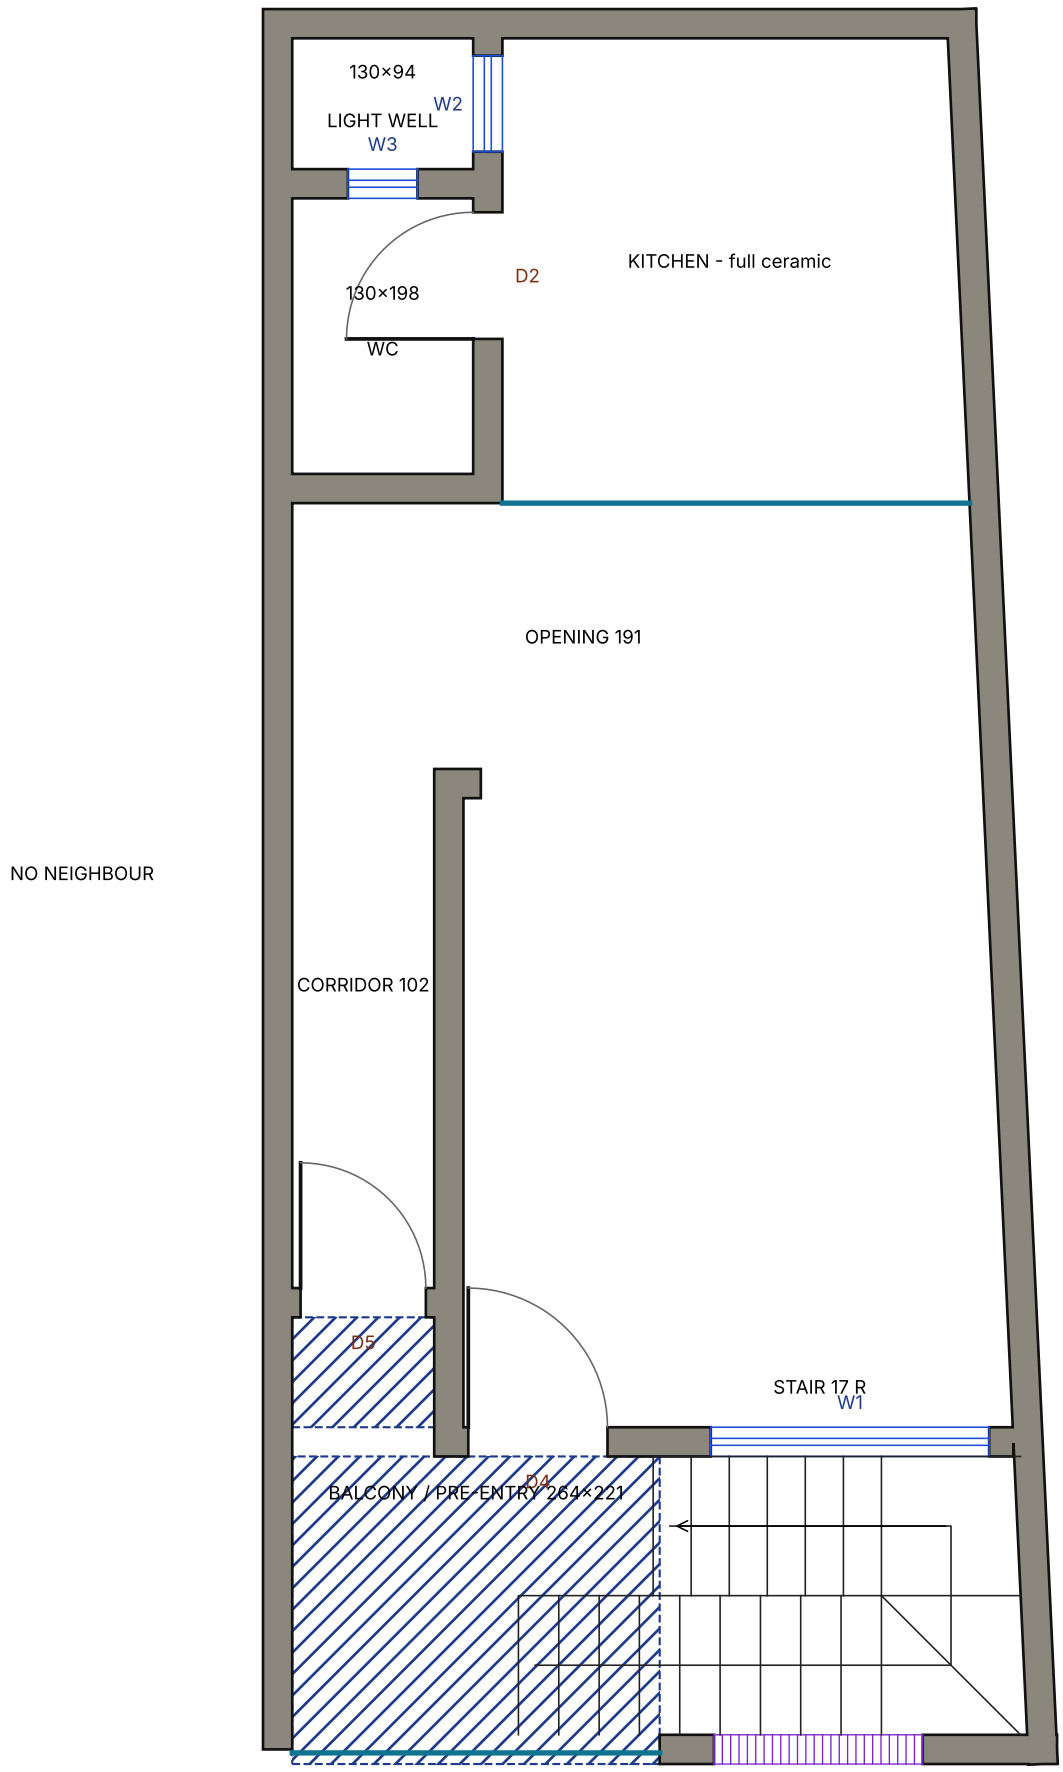


OPENINGS

CNC	screen	W 150	H 300	SILL 0
D4	door	W 100	H 280	SILL 0
D5	door	W 90	H 280	SILL 0
W1	window	W 200	H 210	SILL 90
D2	door	W 91	H 280	SILL 0
W2	window	W 69	H 210	SILL 90
W3	window	W 50	H 60	SILL 195

FIRST FLOOR

units cm | walls 21 | floor-ceiling 300, slab 20 | dimensions from site survey, to be reconciled

DEPTH 1261 from internal dims (site total 1284)

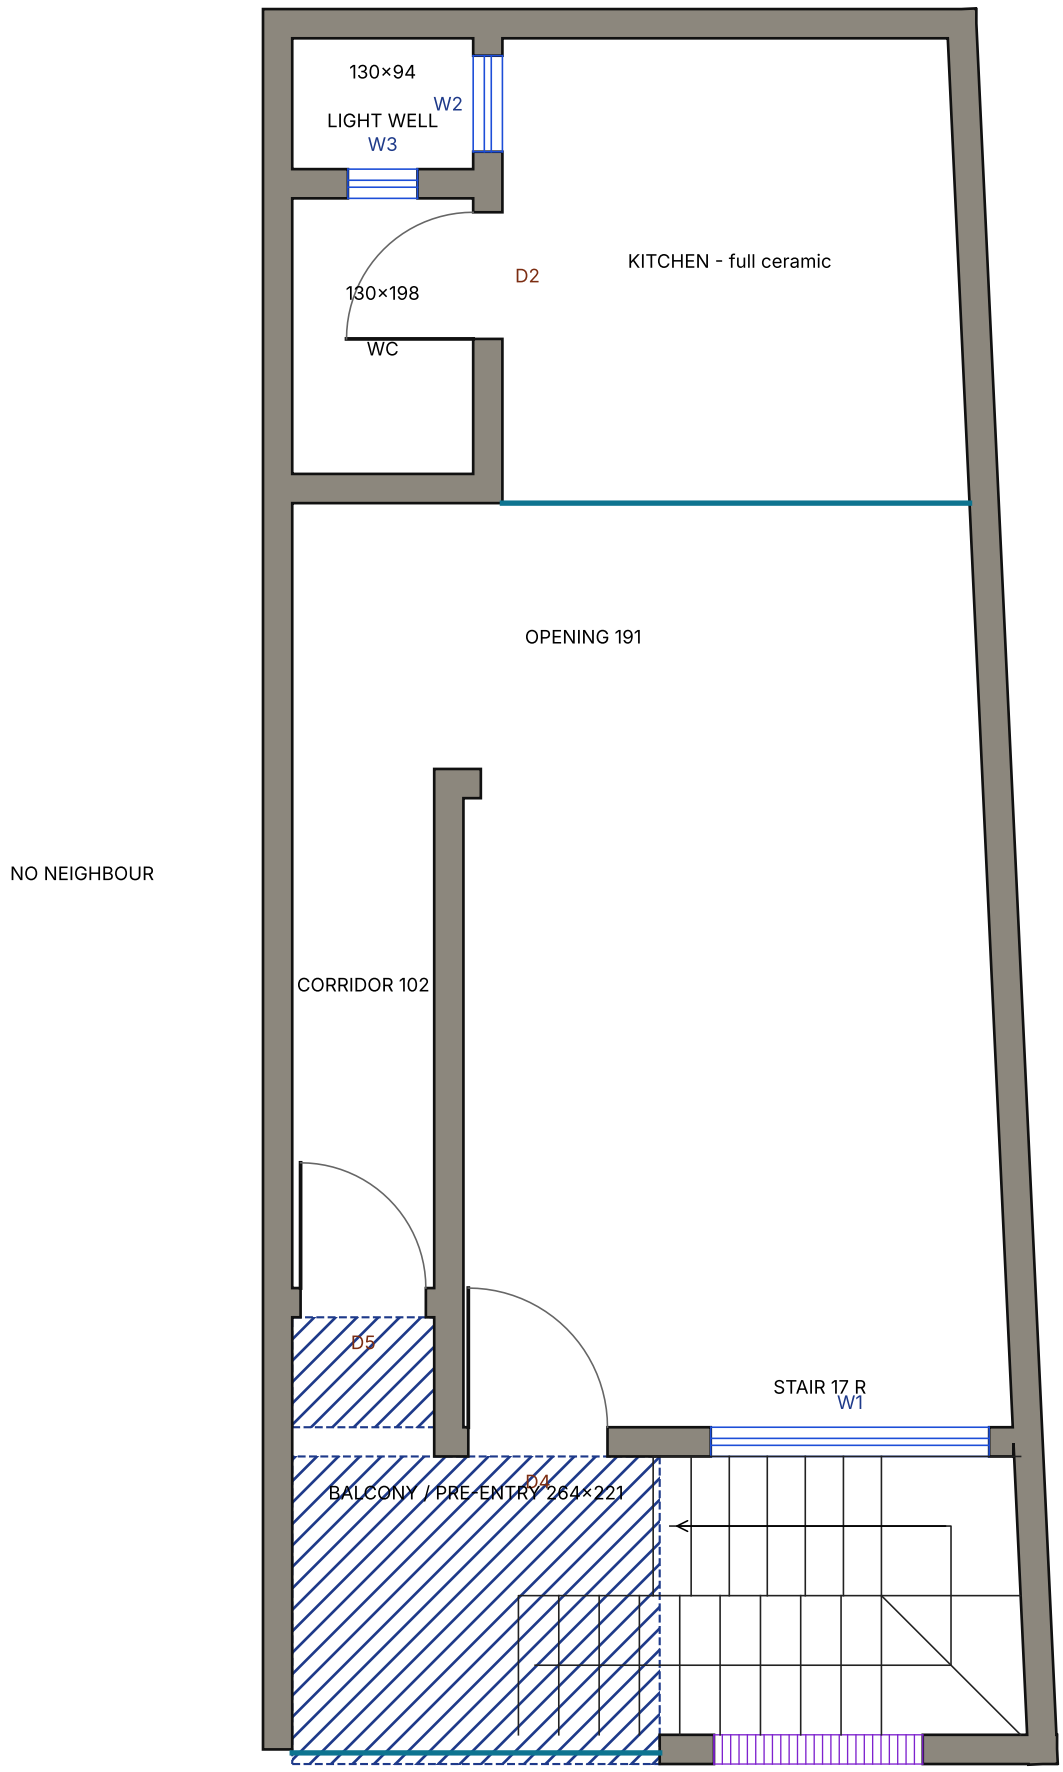


OPENINGS

CNC	screen	W 150	H 300	SILL 0
D4	door	W 100	H 280	SILL 0
D5	door	W 90	H 280	SILL 0
W1	window	W 200	H 210	SILL 90
D2	door	W 91	H 280	SILL 0
W2	window	W 69	H 210	SILL 90
W3	window	W 50	H 60	SILL 195

SECOND FLOOR (typical = first)

units cm | walls 21 | floor-ceiling 300, slab 20 | dimensions from site survey, to be reconciled

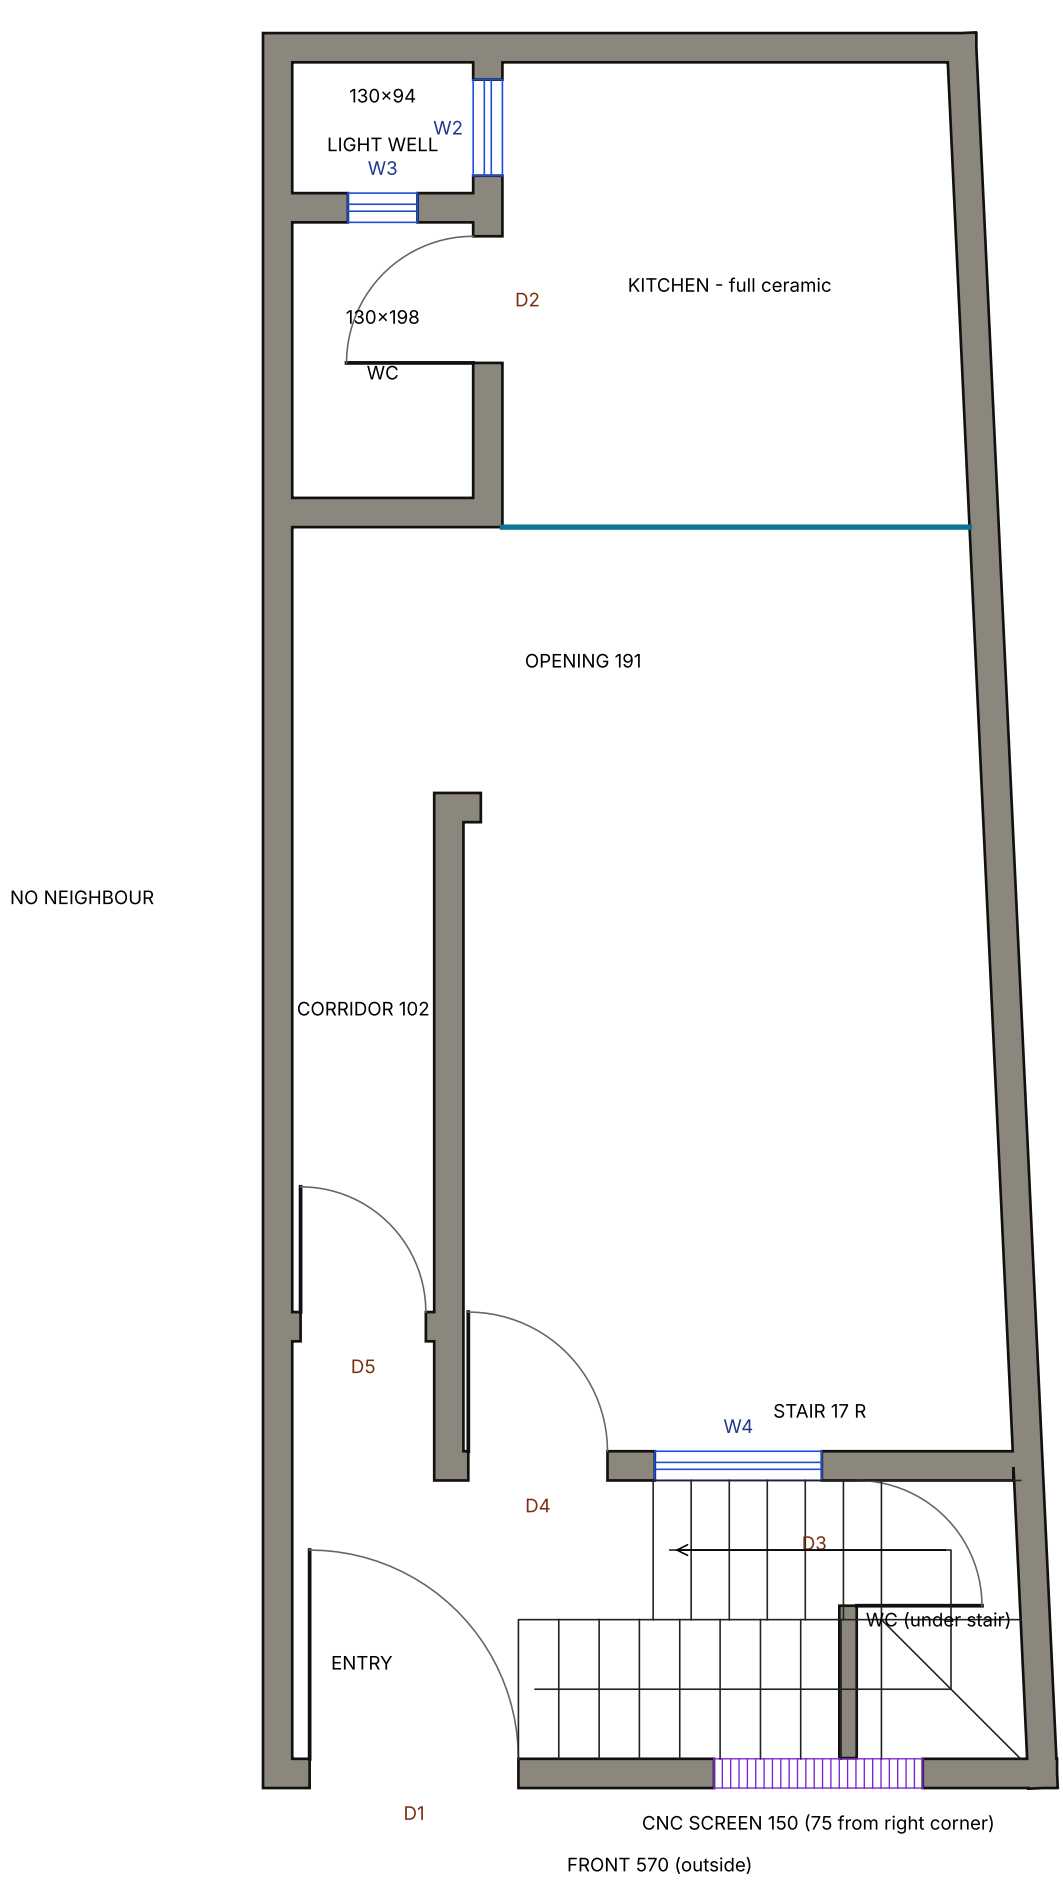


OPENINGS

D1	door	W 150	H 280	SILL 0
CNC	screen	W 150	H to top	SILL 240
D4	door	W 100	H 280	SILL 0
D5	door	W 90	H 280	SILL 0
D2	door	W 91	H 280	SILL 0
W2	window	W 69	H 210	SILL 90
W3	window	W 50	H 60	SILL 195
D3	door	W 90	H 200	SILL 0
W4	window	W 120	H 210	SILL 90

GROUND FLOOR

units cm | walls 21 | floor-ceiling 300, slab 20 | dimensions from site survey, to be reconciled

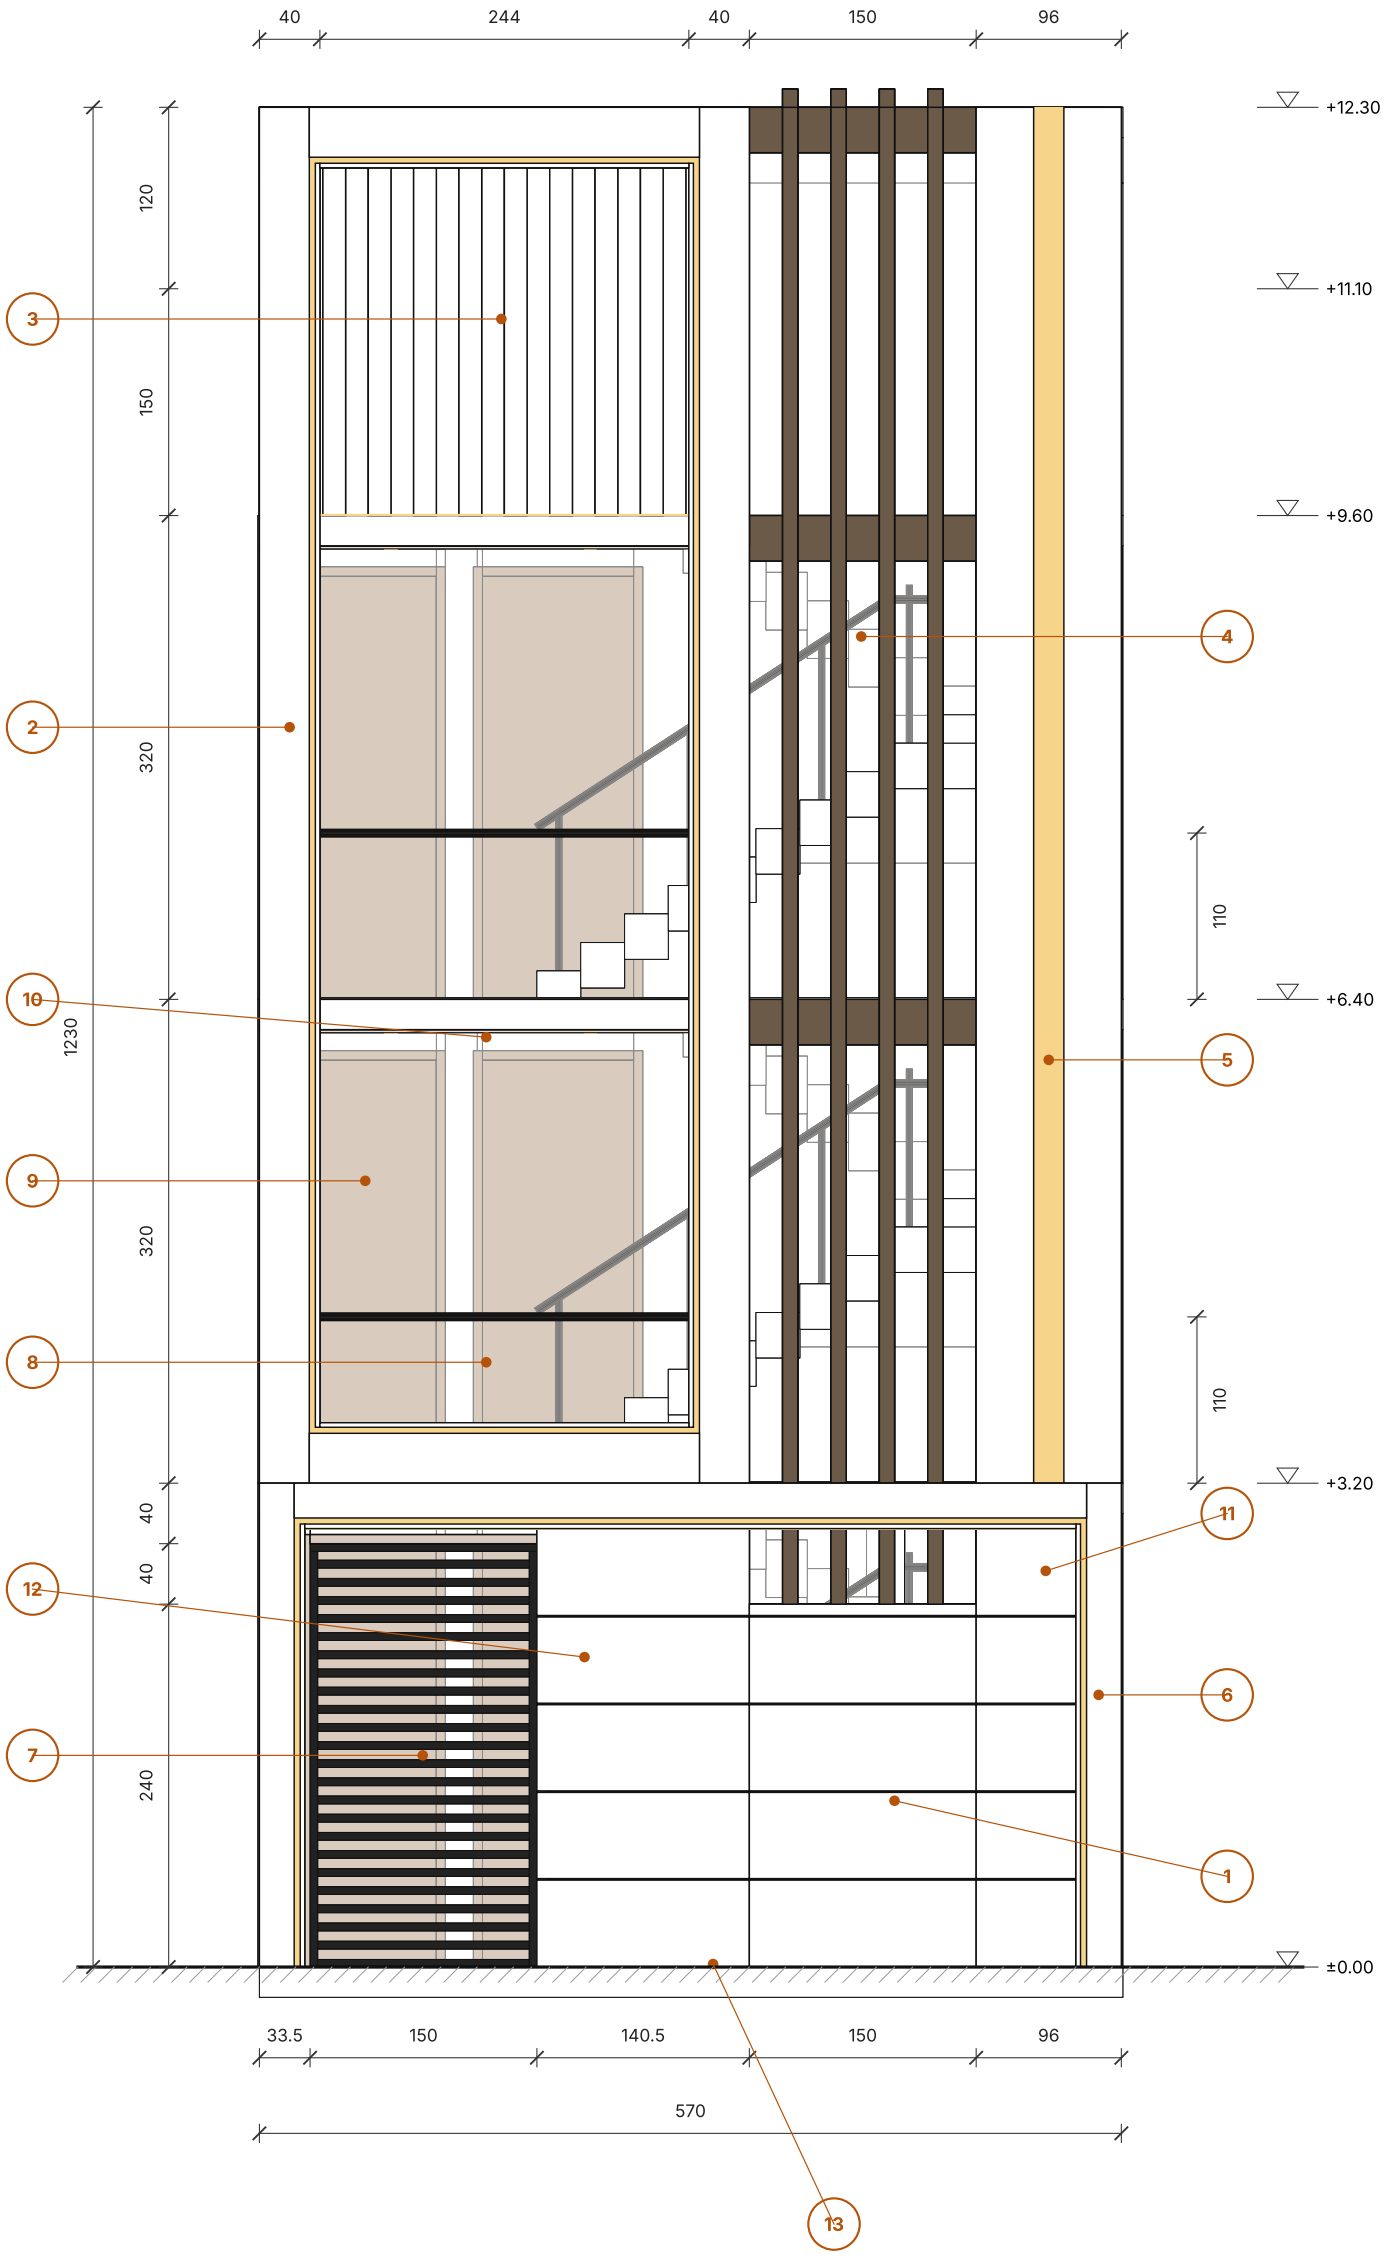

1. Warm cream travertine cladding, horizontal courses, 1 cm joints
   سنگ تراورتن کرم گرم، ردیف افقی، بند ۱ سانت
2. Balcony frame, travertine, face 40, proj. 15 (TBC), recessed LED groove
   قاب بالکن تراورتن، عرض ۴۰، بیرون‌زدگی ۱۵ (تأیید)، شیار نور
3. Ribbed panel: 15 cm strips, alternate ± one stone thickness (3 TBC)
   پنل شیاردار: نوار ۱۵ سانتی، یکی در میان جلو و عقب
4. Bronze vertical bars 10 cm, bands at slab levels, no glass
   میله‌های برنزی ۱۰ سانتی، نوار افقی در تراز دال، بدون شیشه
5. Right pier with vertical recessed LED slot, w 20
   پایهٔ راست با شکاف نوری عمودی، عرض ۲۰
6. Ground frame, face 30, proj. 35 (TBC), recessed LED groove
   قاب همکف، عرض ۳۰، بیرون‌زدگی ۳۵ (تأیید)، شیار نور
7. Gate 150 × 280, black metal horizontal flat bars, open gaps
   درِ ورودی ۱۵۰ × ۲۸۰، تسمهٔ افقی فلزی مشکی با فاصلهٔ باز
8. Frameless glass balustrade h 110, bronze tube top rail
   نردهٔ شیشه‌ای ۱۱۰ با دستگیرهٔ لوله‌ای برنزی
9. Walnut doors 90/100 × 280 (corridor door recessed 1 m)
   درهای گردو ۹۰ و ۱۰۰ × ۲۸۰ (درِ راهرو ۱ متر عقب)
10. Wood soffit with recessed downlights
    سقف چوبی با چراغ توکار
11. House number "11", brushed bronze (position per render, TBC)
    پلاک «۱۱» برنزی (جا طبق رندر، تأیید)
12. Up/down wall light, dark bronze (TBC)
    چراغ دیواری دوطرفه برنزی (تأیید)
13. In-ground uplights ×3 at base of ground frame (TBC)
    ۳ چراغ کف‌خواب پای قاب همکف (تأیید)

ArchTverse · KARBALA HOUSE 5.70 × 12.84 — **SCALE 1:50 @ A3**

FRONT ELEVATION — dimensioned | units: cm | levels: m | from design model (plan_*.dxf)

TBC: frame projections 15 / 35, stone thickness 3, gate bars 5/7, fixtures 11–13 positions